Implantación y techos

A-01



PROYECTO	UBICACIÓN	CONTENIDO	ESCALA	SUPERFICIE	LÁMINA
Casa Yerko 250 m²	**Terreno de 12,00 × 25,00 m · 300 m²**	**Implantación y techos**	**1:100**	**249,70 m² cubiertos**	**A-01**

Retiro frontal 3,00 m · retiros laterales 0,50 m · patio posterior 10,00 m · ocupación 132,00 m² (44 % del terreno).

Planta baja

A-02




PROYECTO	UBICACIÓN	CONTENIDO	ESCALA	SUPERFICIE	LÁMINA
Casa Yerko 250 m²	**Terreno de 12,00 × 25,00 m · 300 m²**	**Planta baja**	**1:100**	**249,70 m² cubiertos**	**A-02**

Superficie 132,00 m². Altura libre 2,70 m. Muros de 0,20 m acotados a ejes. Escalera de 18 contrapasos de 0,175 m y pisada de 0,28 m.

Planta alta

A-03

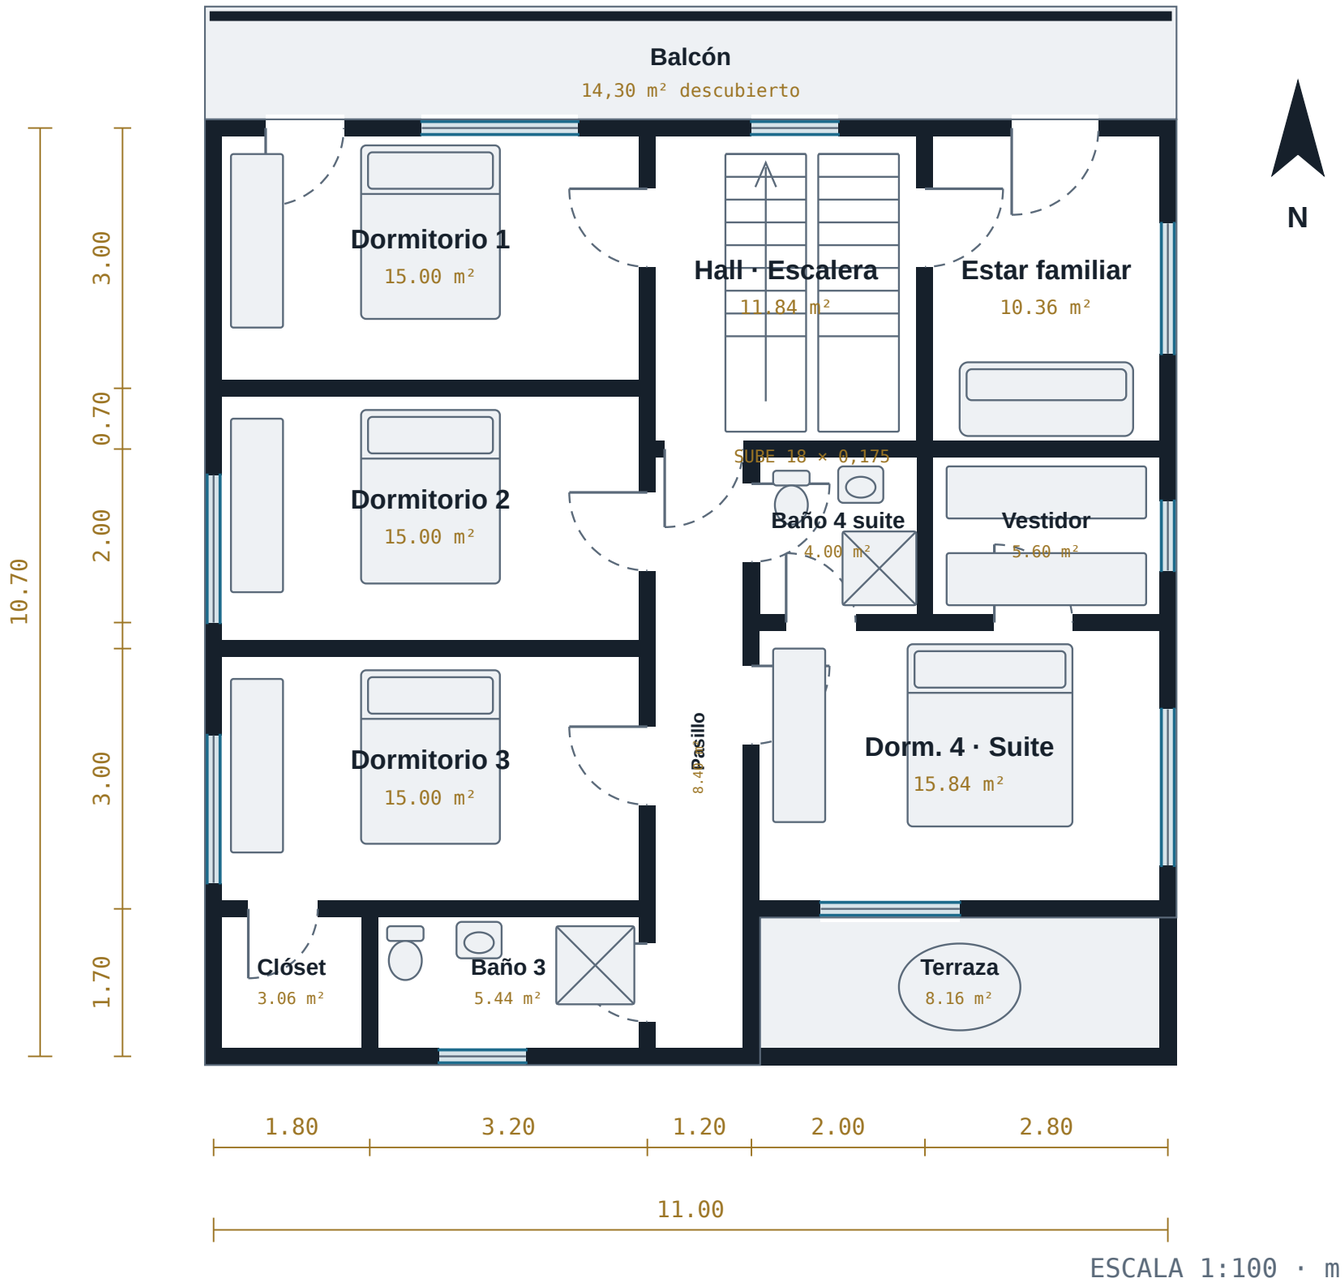

ESCALA 1:100 · m


PROYECTO	UBICACIÓN	CONTENIDO	ESCALA	SUPERFICIE	LÁMINA
Casa Yerko 250 m²	**Terreno de 12,00 × 25,00 m · 300 m²**	**Planta alta**	**1:100**	**249,70 m² cubiertos**	**A-03**

Superficie 117,70 m² (incluye terraza cubierta de 8,16 m²). Balcón descubierto de 14,30 m². Altura libre 2,60 m.

Fachadas


A-04

FACHADA FRONTAL · CALLE

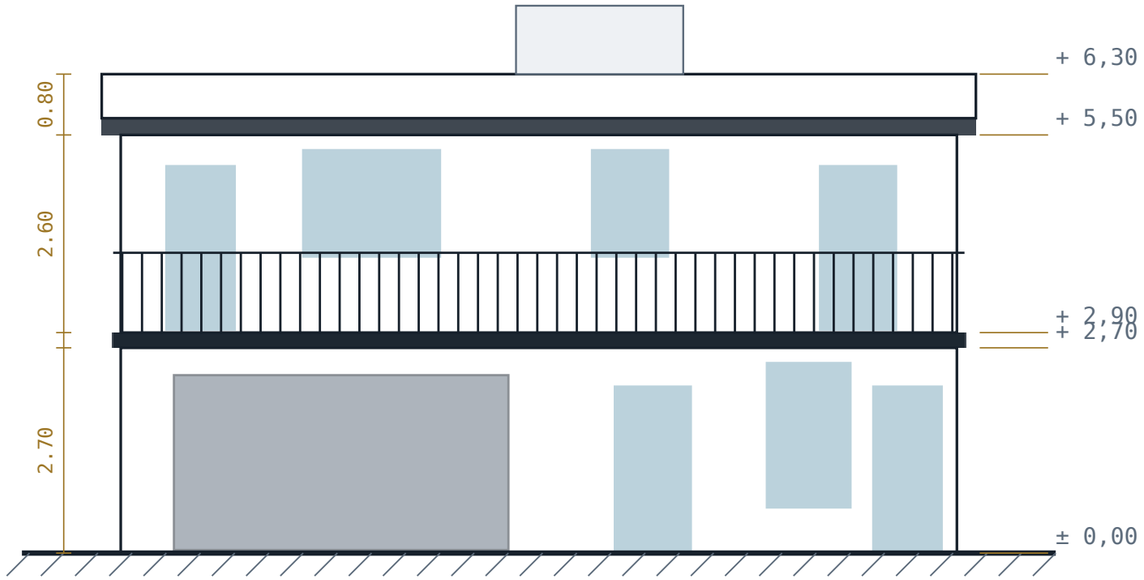


FACHADA FRONTAL · CALLE · ESC 1:100

FACHADA POSTERIOR · PATIO

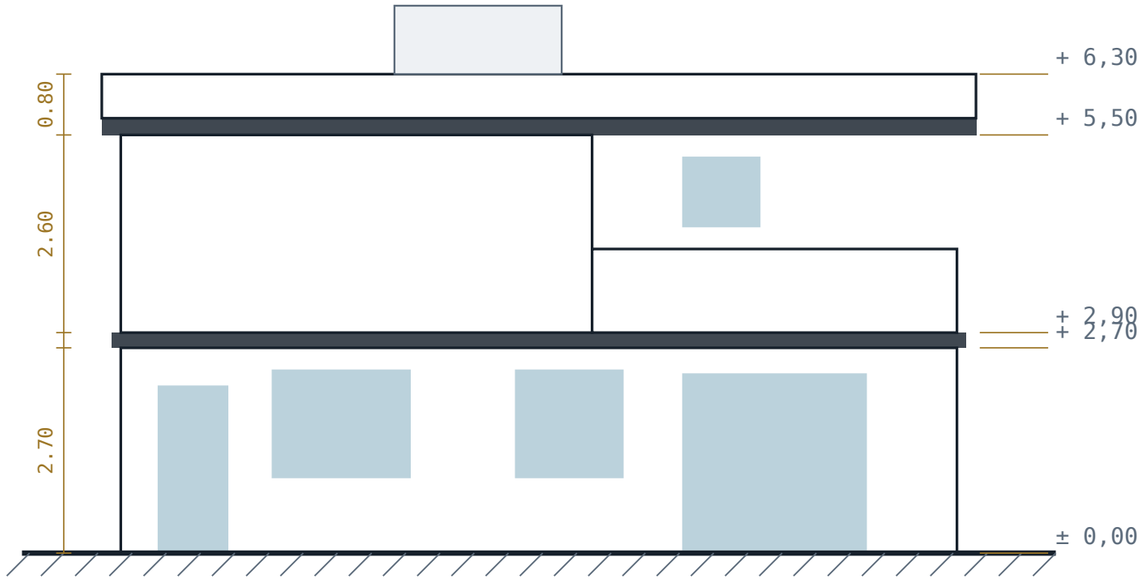


FACHADA POSTERIOR · PATIO · ESC 1:100

FACHADA LATERAL DERECHA

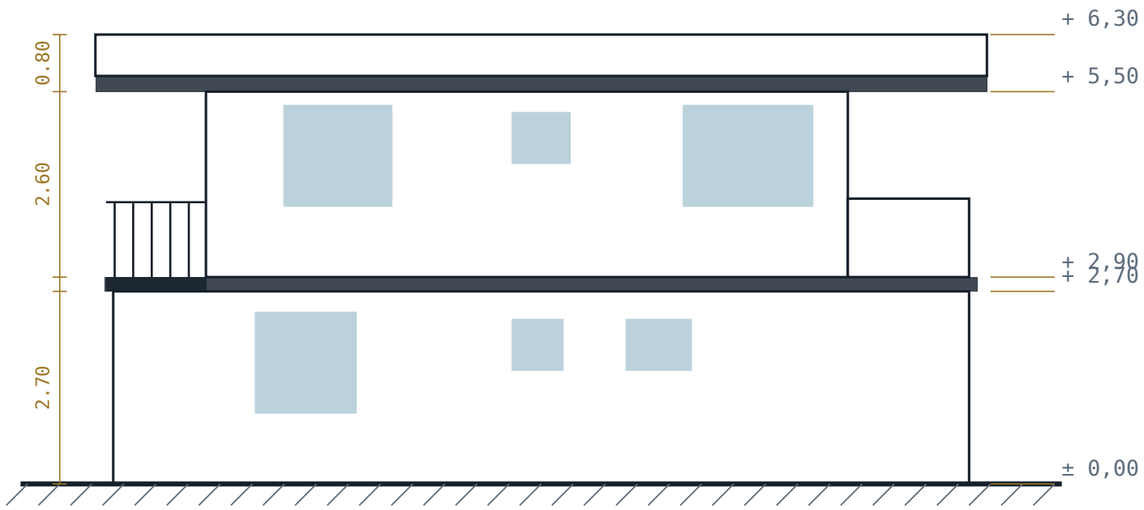

FACHADA LATERAL DERECHA · ESC 1:100

FACHADA LATERAL IZQUIERDA

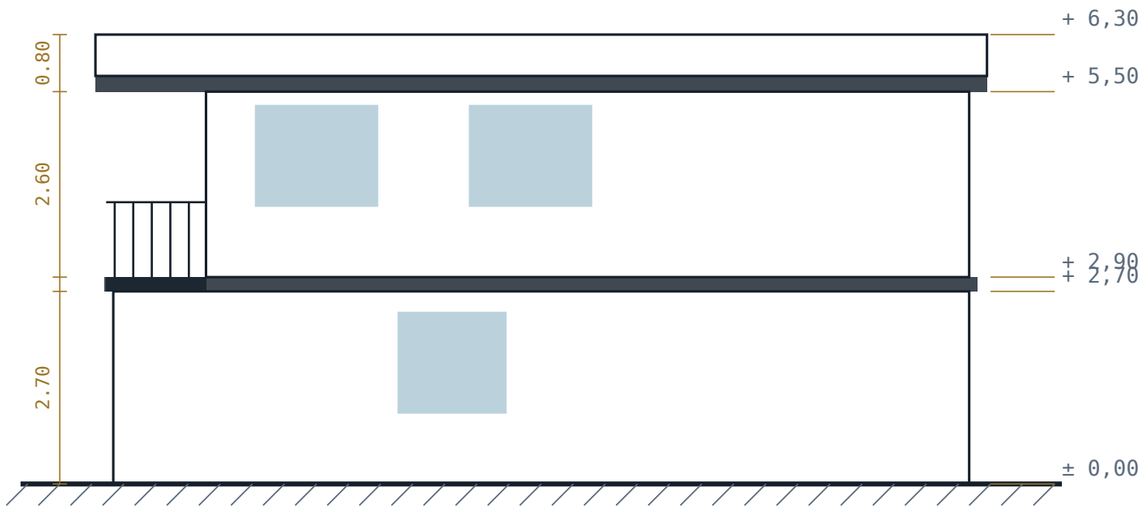


FACHADA LATERAL IZQUIERDA · ESC 1:100

PROYECTO	UBICACIÓN	CONTENIDO	ESCALA	SUPERFICIE	LÁMINA
Casa Yerko 250 m²	**Terreno de 12,00 × 25,00 m · 300 m²**	**Fachadas norte, sur, este y oeste**	**1:100**	**249,70 m² cubiertos**	**A-04**

Niveles: ± 0,00 piso terminado · + 2,70 losa de entrepiso · + 2,90 piso alto · + 5,50 losa de cubierta · + 6,30 parapeto · + 7,42 tanque de reserva.

Axonometría del conjunto

A-05

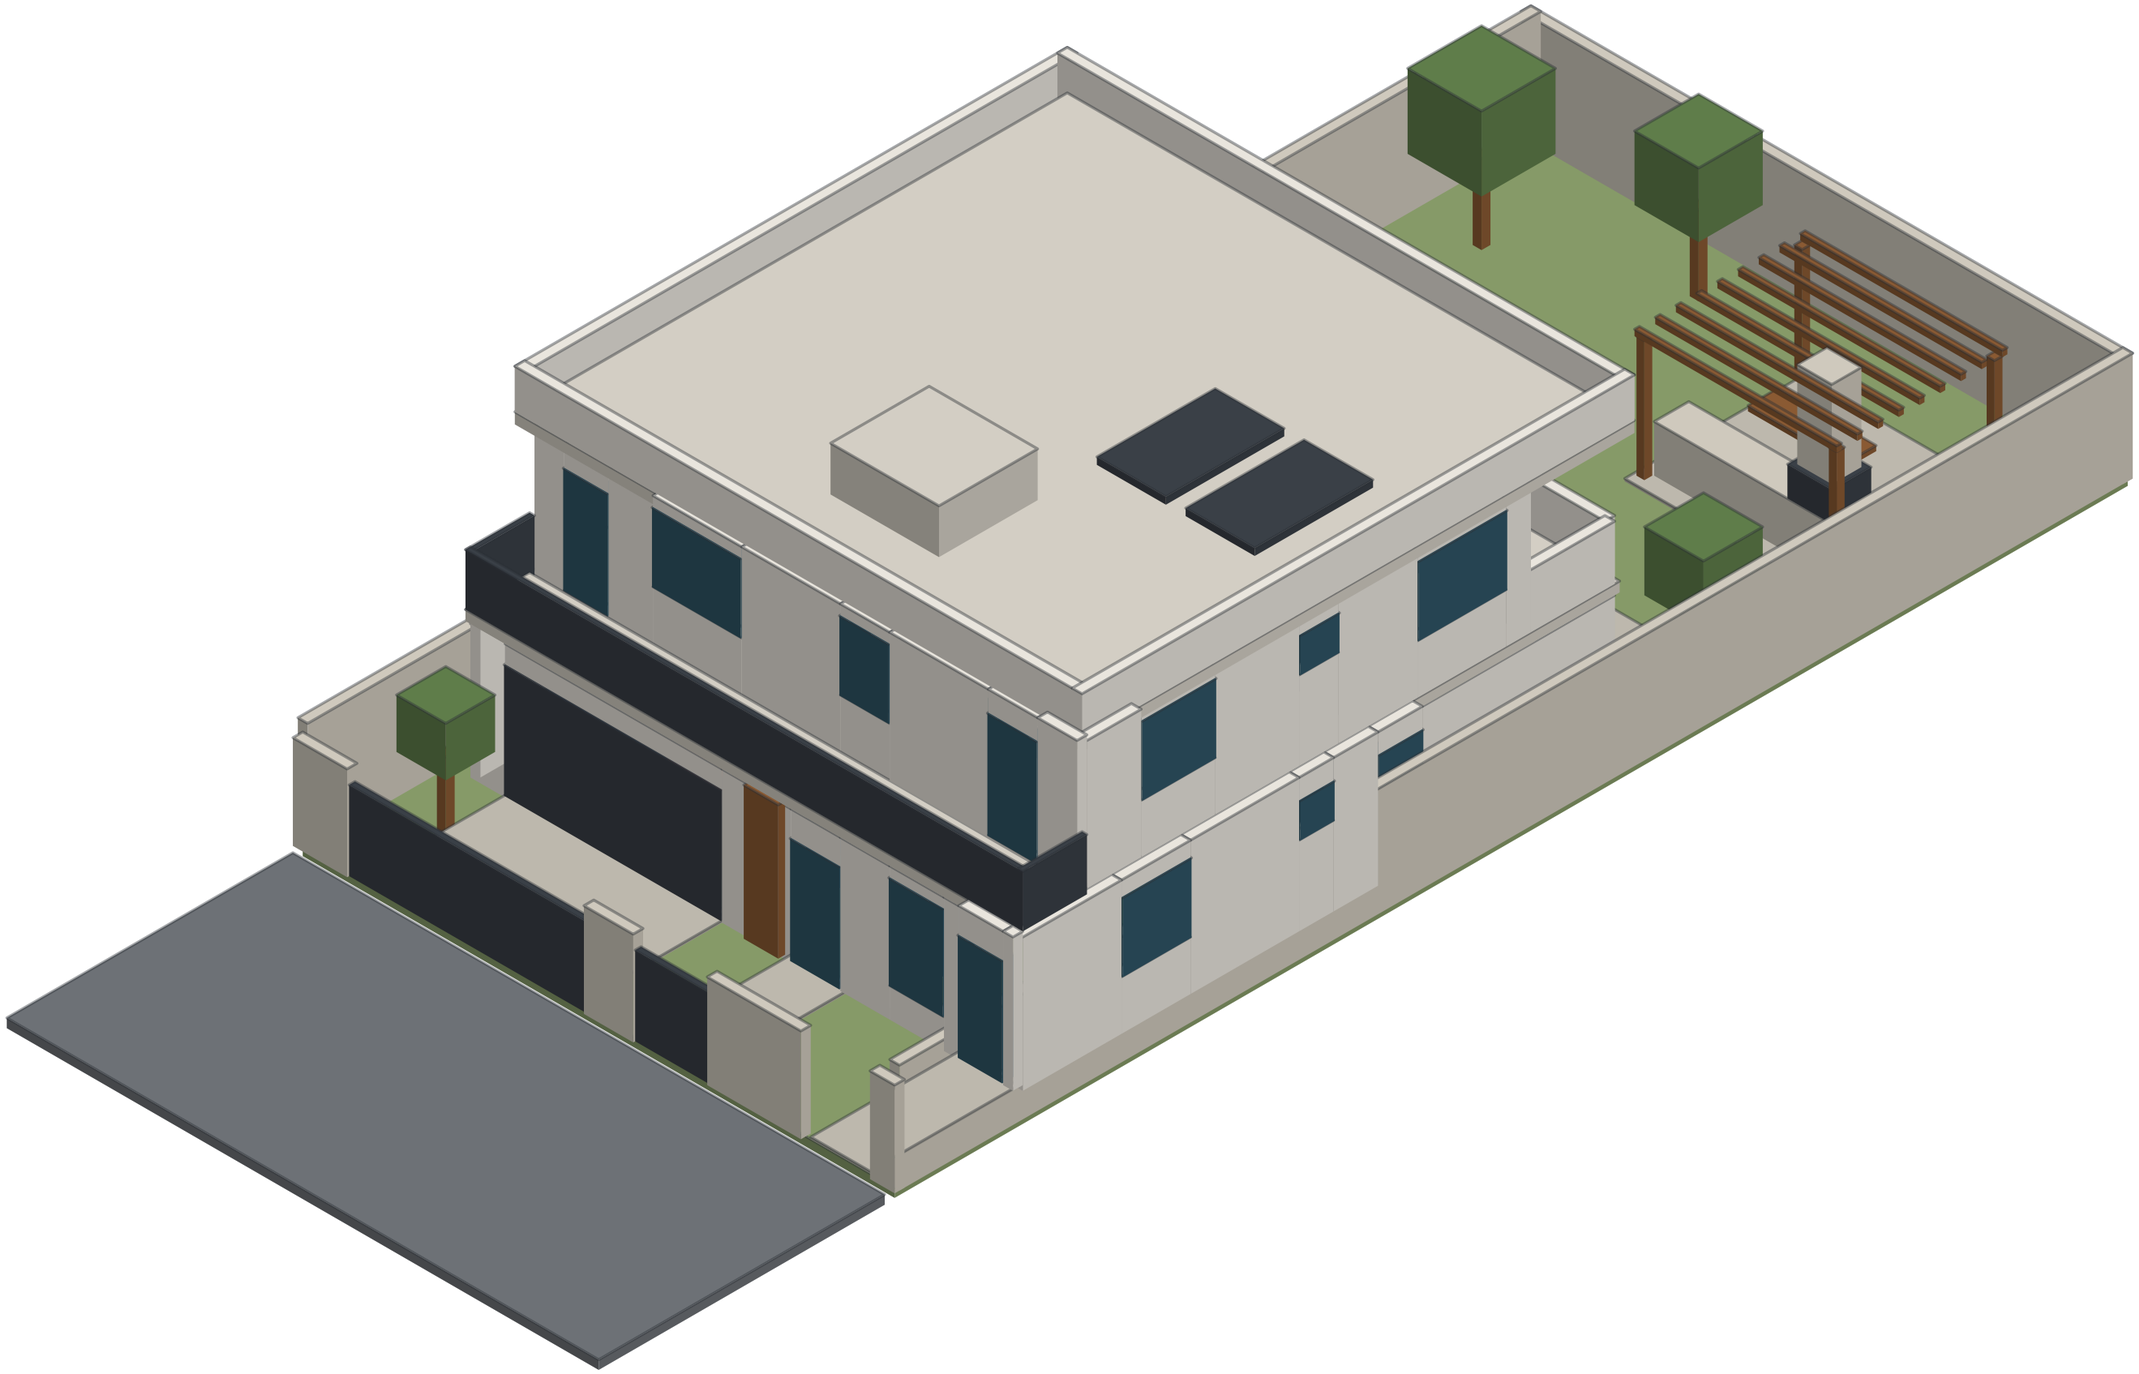

PROYECTO	UBICACIÓN	CONTENIDO	ESCALA	SUPERFICIE	LÁMINA
Casa Yerko 250 m²	**Terreno de 12,00 × 25,00 m · 300 m²**	**Axonometría del conjunto**	**sin escala**	**249,70 m² cubiertos**	**A-05**

Vista desde la calle. Cubierta plana con parapeto de 0,80 m, tanque de reserva sobre la caja de escalera y previsión de seis paneles fotovoltaicos.

Cuadro de áreas y resumen de presupuesto

A-06

Planta baja

AMBIENTE	MEDIDAS (M)	M²
Garaje 2 autos	5.60 × 5.00	28.00
Hall · Escalera	2.60 × 5.00	13.00
Tienda	2.80 × 5.00	14.00
Sala – Comedor	6.20 × 7.00	43.40
Pasillo	1.40 × 3.40	4.76
Baño 1	1.70 × 1.90	3.23
Baño 2 servicio	1.70 × 1.90	3.23
Lavandería	3.40 × 1.50	5.10
Cocina	4.80 × 3.60	17.28
Total		**132.00**

Planta alta

AMBIENTE	MEDIDAS (M)	M²
Dormitorio 1	5.00 × 3.00	15.00
Hall · Escalera	3.20 × 3.70	11.84
Estar familiar	2.80 × 3.70	10.36
Dormitorio 2	5.00 × 3.00	15.00
Pasillo	1.20 × 7.00	8.40
Baño 4 suite	2.00 × 2.00	4.00
Vestidor	2.80 × 2.00	5.60
Dormitorio 3	5.00 × 3.00	15.00
Dorm. 4 · Suite	4.80 × 3.30	15.84
Clóset	1.80 × 1.70	3.06
Baño 3	3.20 × 1.70	5.44
Terraza	4.80 × 1.70	8.16
Total		**117.70**

Resumen de presupuesto

CAP.	DESCRIPCIÓN	BS
1	TRABAJOS PRELIMINARES	9.699,37
2	MOVIMIENTO DE TIERRAS	13.509,21
3	OBRA GRUESA: HORMIGONES Y ESTRUCTURA	260.231,64
4	MAMPOSTERÍA Y CERRAMIENTOS	96.266,77
5	REVOQUES, CIELOS Y PINTURA	125.740,19
6	PISOS Y REVESTIMIENTOS	99.311,04
7	CUBIERTA	27.833,44
8	CARPINTERÍA	126.403,39
9	INSTALACIÓN SANITARIA Y AGUA	56.558,77
10	INSTALACIÓN ELÉCTRICA	50.101,33
11	OBRAS EXTERIORES	111.342,03
	TOTAL PRESUPUESTO	**976.997,18**
	Costo por m² cubierto	3.912,68

PROYECTO	UBICACIÓN	CONTENIDO	ESCALA	SUPERFICIE	LÁMINA
Casa Yerko 250 m²	**Terreno de 12,00 × 25,00 m · 300 m²**	**Cuadro de áreas y resumen de presupuesto**	**s/esc**	**249,70 m² cubiertos**	**A-06**

Superficies medidas sobre ejes de muro. Presupuesto referencial en bolivianos, estructura de precios unitarios con 55 % de cargas sociales, 10 % de gastos generales, 7 % de utilidad y 3,09 % de IT.